


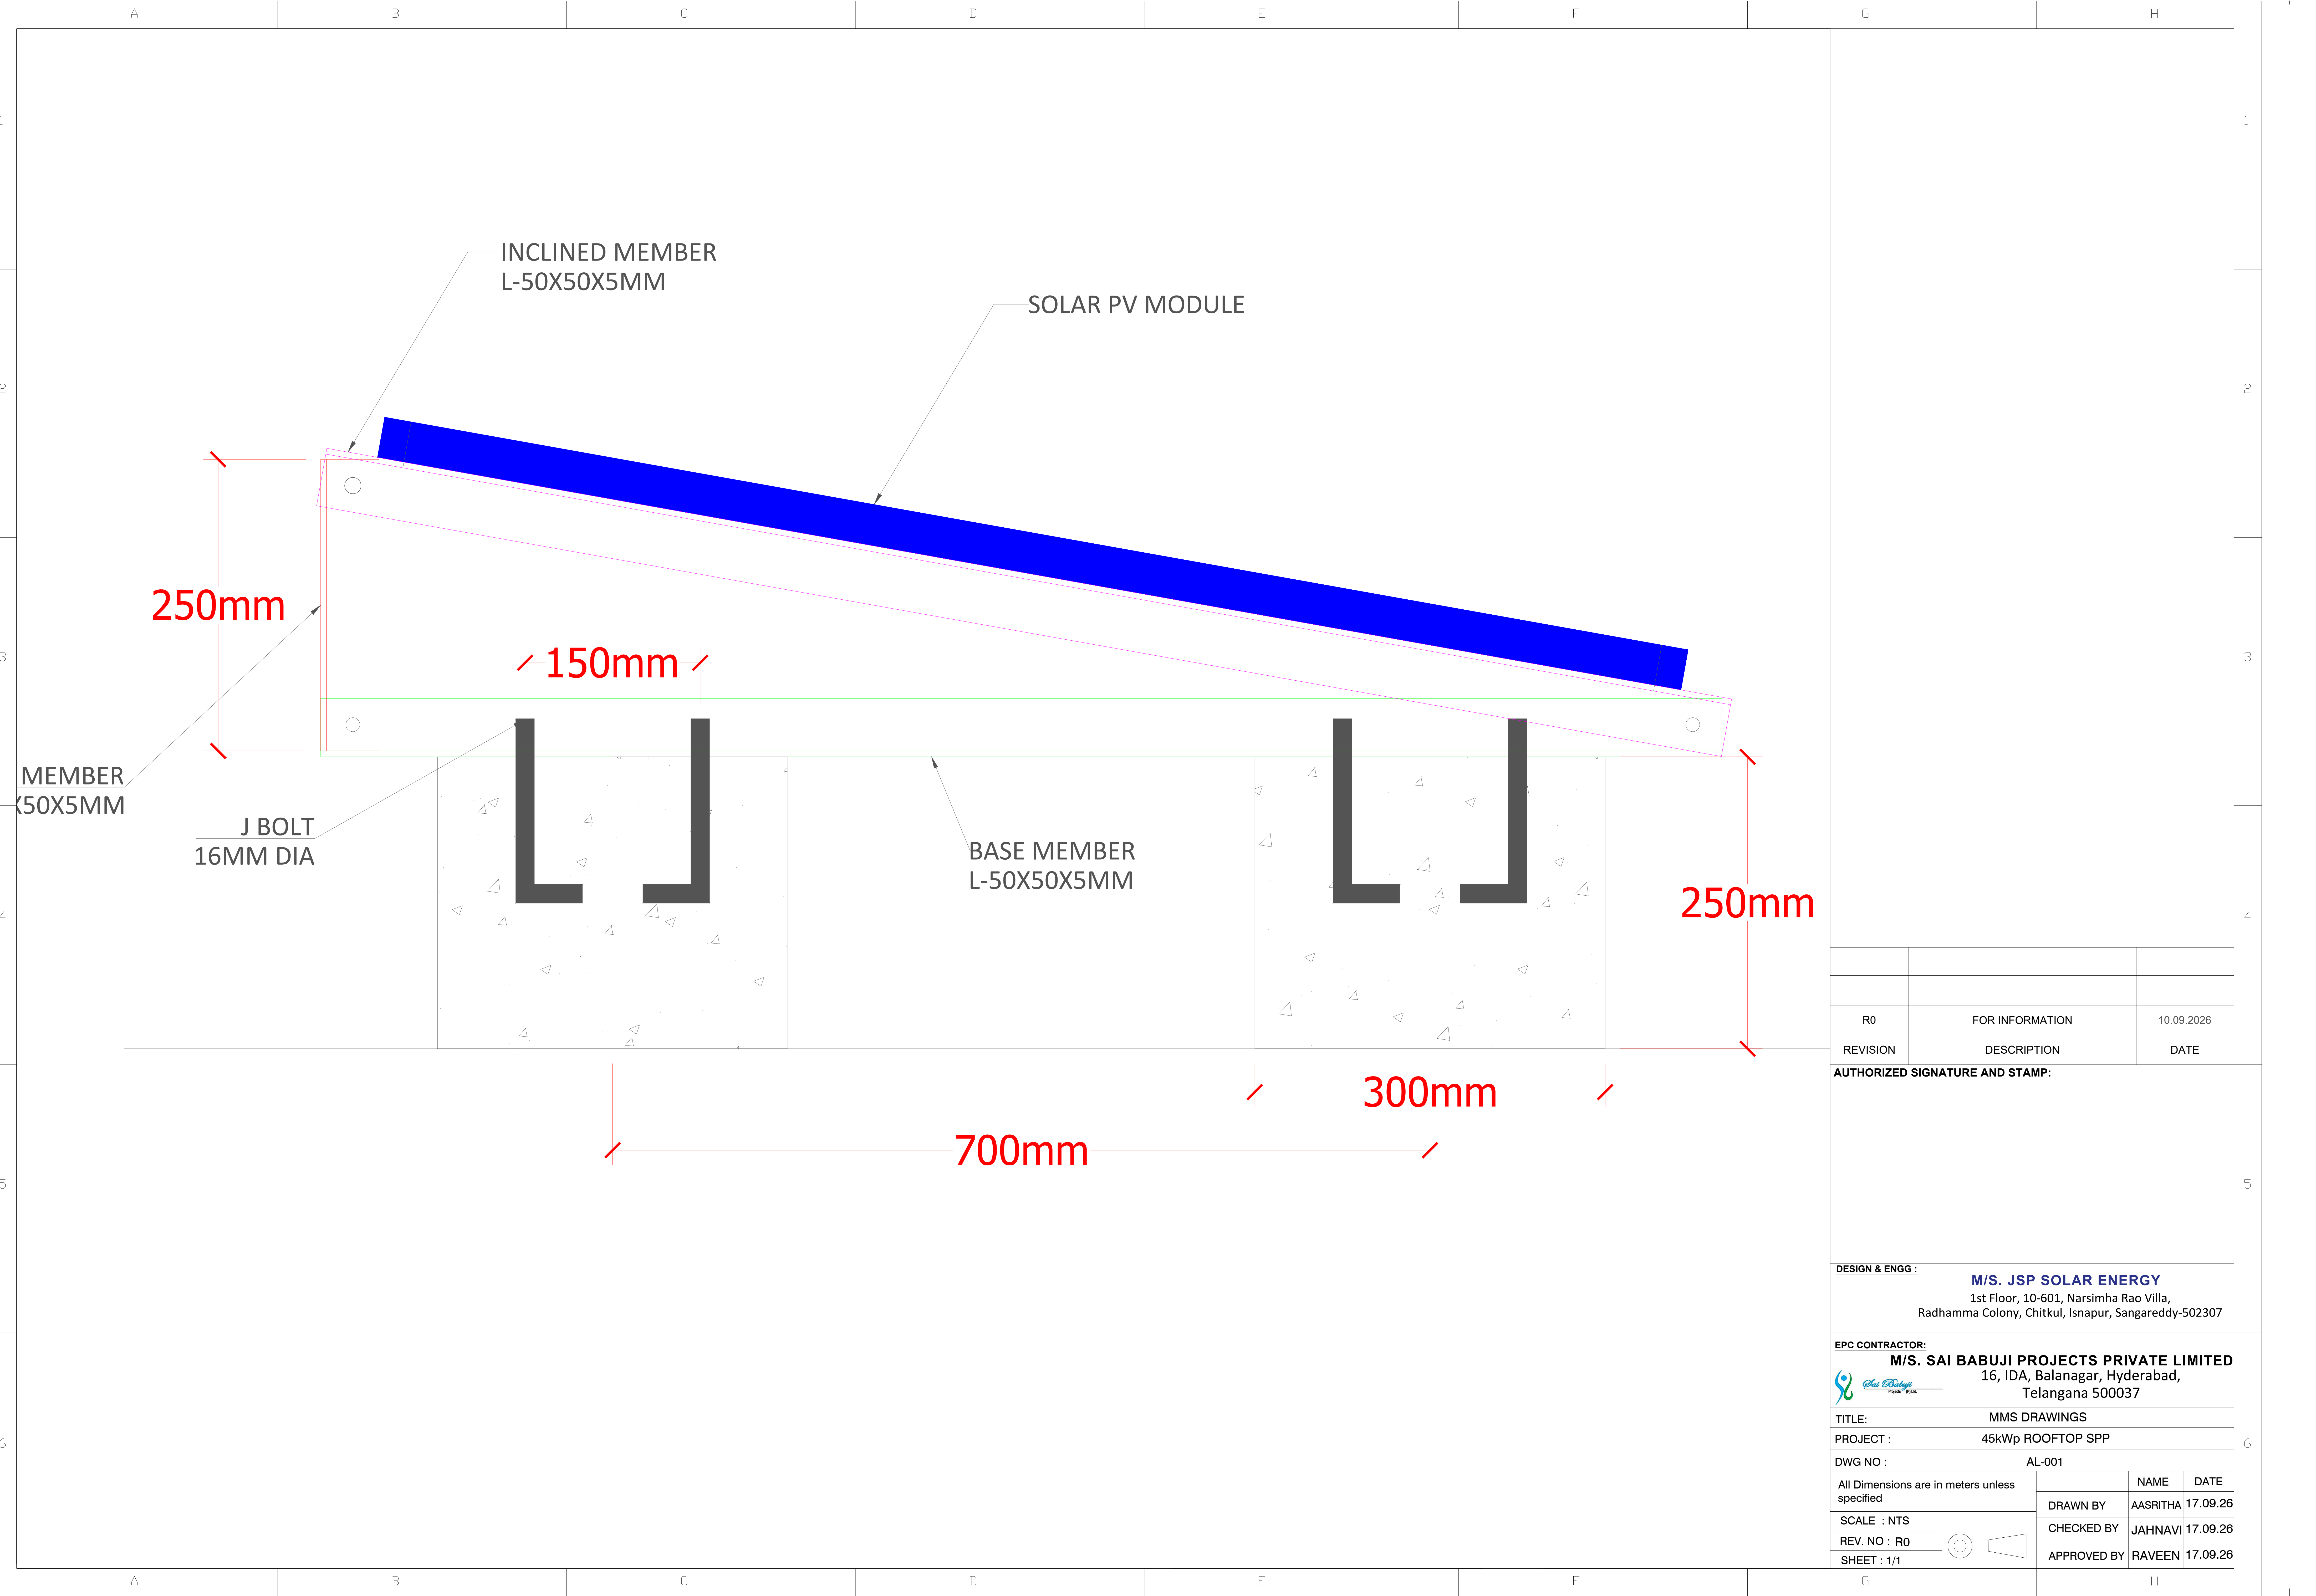

R0	FOR INFORMATION	10.09.2026
REVISION	DESCRIPTION	DATE

AUTHORIZED SIGNATURE AND STAMP:

DESIGN & ENGG :
M/S. JSP SOLAR ENERGY
1st Floor, 10-601, Narsimha Rao Villa,
Radhamma Colony, Chitkul, Isnapur, Sangareddy-502307

EPC CONTRACTOR:
M/S. SAI BABUJI PROJECTS PRIVATE LIMITED
16, IDA, Balanagar, Hyderabad,
Telangana 500037

TITLE: MMS DRAWINGS

PROJECT : 45kWp ROOFTOP SPP

DWG NO : AL-001

All Dimensions are in meters unless specified		NAME	DATE
SCALE : NTS		DRAWN BY	AASRITHA 17.09.26
REV. NO : R0		CHECKED BY	JAHNAVI 17.09.26
SHEET : 1/1		APPROVED BY	RAVEEN 17.09.26

